
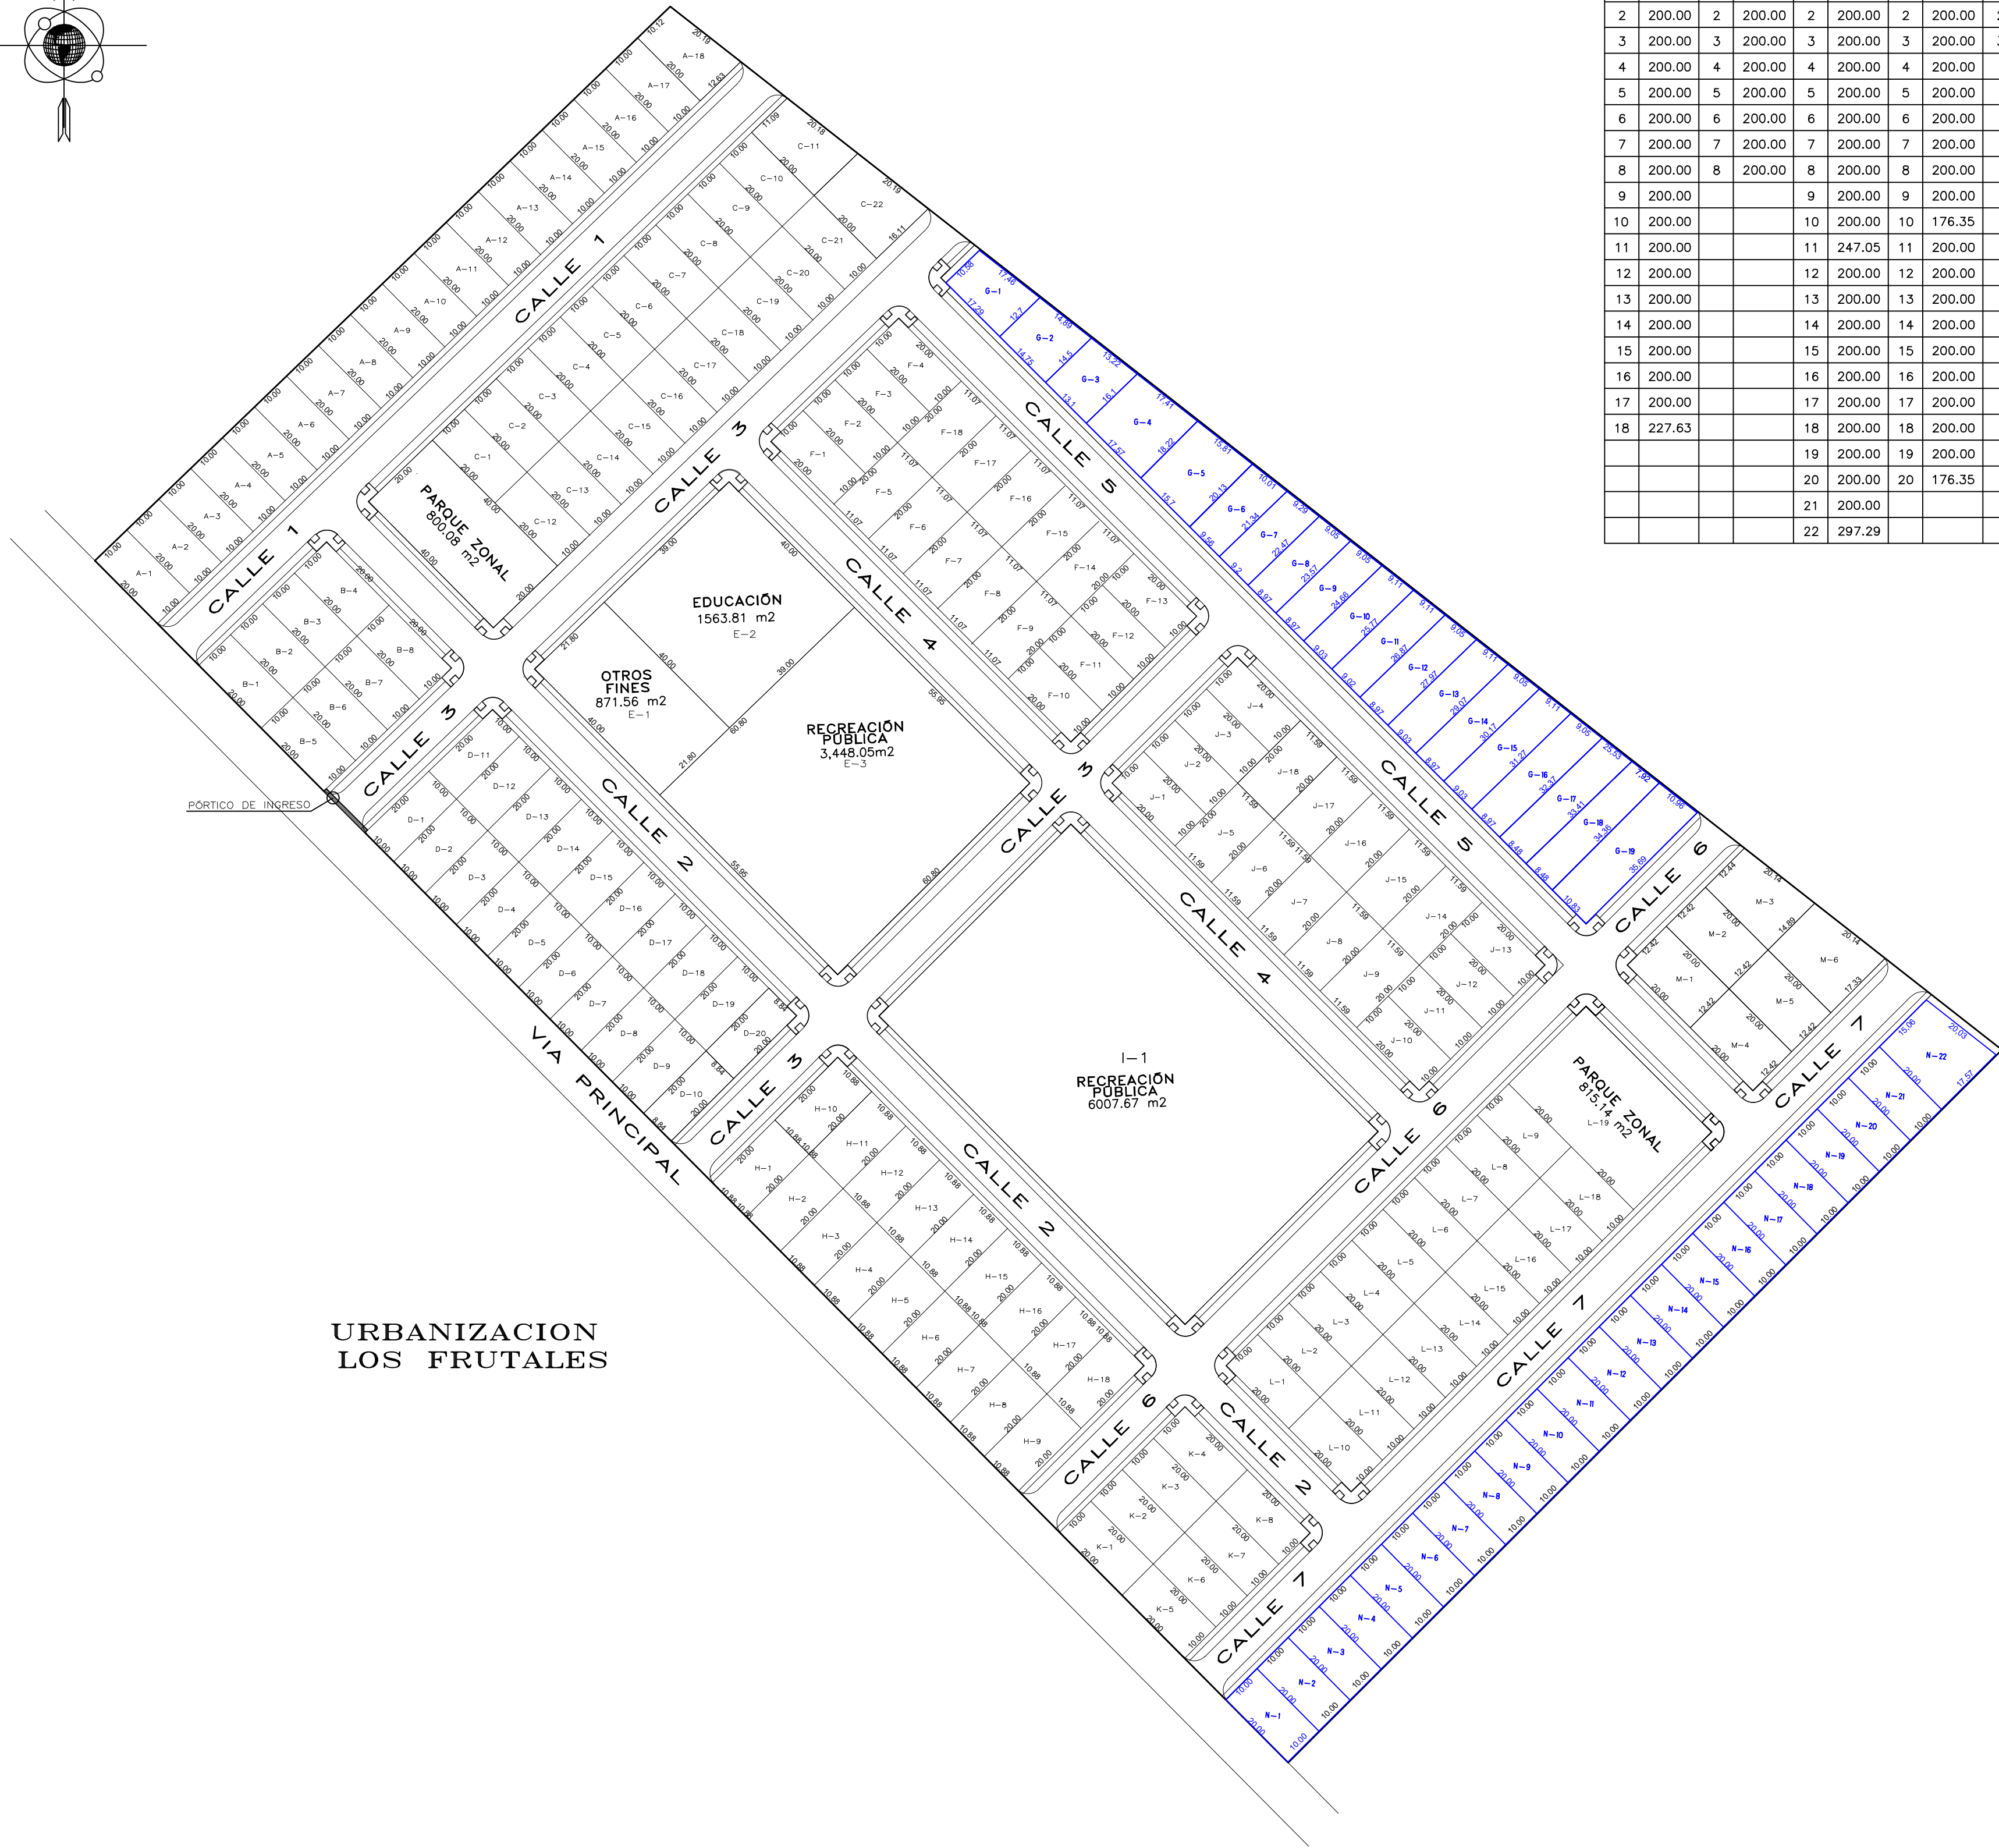


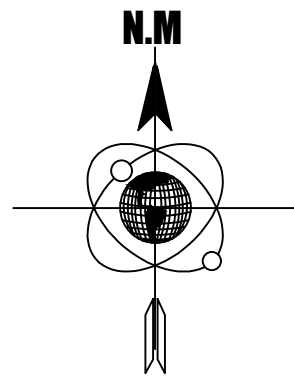

Mz. A		Mz. B		Mz. C		Mz. D		Mz. E		Mz. F		Mz. G		Mz. H		Mz. I		Mz. J		Mz. K		Mz. L		Mz. M		Mz. N	
Lote	Área	Lote	Área	Lote	Área	Lote	Área	Lote	Área	Lote	Área	Lote	Área	Lote	Área	Lote	Área	Lote	Área	Lote	Área	Lote	Área	Lote	Área	Lote	Área
1	200.00	1	200.00	1	200.00	1	200.00	1	871.56	1	200.00	1	201.21	1	217.59	1	6007.67	1	200.00	1	200.00	1	200.00	1	248.38	1	200.00
2	200.00	2	200.00	2	200.00	2	200.00	2	1563.81	2	200.00	2	200.53	2	217.59			2	200.00	2	200.00	2	200.00	2	248.40	2	200.00
3	200.00	3	200.00	3	200.00	3	200.00	3	3448.05	3	200.00	3	200.36	3	217.59			3	200.00	3	200.00	3	200.00	3	273.41	3	200.00
4	200.00	4	200.00	4	200.00	4	200.00			4	200.00	4	298.77	4	217.59			4	200.00	4	200.00	4	200.00	4	248.38	4	200.00
5	200.00	5	200.00	5	200.00	5	200.00			5	221.40	5	300.93	5	217.59			5	231.80	5	200.00	5	200.00	5	248.40	5	200.00
6	200.00	6	200.00	6	200.00	6	200.00			6	221.40	6	202.06	6	217.59			6	231.80	6	200.00	6	200.00	6	322.19	6	200.00
7	200.00	7	200.00	7	200.00	7	200.00			7	221.40	7	201.56	7	217.59			7	231.80	7	200.00	7	200.00			7	200.00
8	200.00	8	200.00	8	200.00	8	200.00			8	221.40	8	206.36	8	217.59			8	231.80	8	200.00	8	200.00			8	200.00
9	200.00			9	200.00	9	200.00			9	221.40	9	216.20	9	217.59			9	231.80			9	200.00			9	200.00
10	200.00			10	200.00	10	176.35			10	200.00	10	227.58	10	217.59			10	200.00			10	200.00			10	200.00
11	200.00			11	247.05	11	200.00			11	200.00	11	237.48	11	217.59			11	200.00			11	200.00			11	200.00
12	200.00			12	200.00	12	200.00			12	200.00	12	245.84	12	217.59			12	200.00			12	200.00			12	200.00
13	200.00			13	200.00	13	200.00			13	200.00	13	257.41	13	217.59			13	200.00			13	200.00			13	200.00
14	200.00			14	200.00	14	200.00			14	221.40	14	265.57	14	217.59			14	231.80			14	200.00			14	200.00
15	200.00			15	200.00	15	200.00			15	221.40	15	277.22	15	217.59			15	231.80			15	200.00			15	200.00
16	200.00			16	200.00	16	200.00			16	221.40	16	285.31	16	217.59			16	231.80			16	200.00			16	200.00
17	200.00			17	200.00	17	200.00			17	221.40	17	278.89	17	217.59			17	231.80			17	200.00			17	200.00
18	227.63			18	200.00	18	200.00			18	221.40	18	276.71	18	217.59			18	231.80			18	200.00			18	200.00
				19	200.00	19	200.00					19	380.21								19	815.14			19	200.00	
				20	200.00	20	176.35																	20		20	200.00
				21	200.00																		21		21	200.00	
				22	297.29																		22		22	326.30	

PROYECTO:

URBANIZACIÓN
LOS FRUTALES
DEL DISTRITO DE LA JOYA
DEPARTAMENTO DE
AREQUIPA

UBICACIÓN:

DEPARTAMENTO: AREQUIPA
PROVINCIA: AREQUIPA
DISTRITO: LA JOYA
LUGAR: SAN ISIDRO

PROPIETARIO:

ALMAREN

PLANO:

PLANIMETRIA
GENERAL

PG

ESCALA: 1/1000

FECHA: FEBRERO 2024